


PROYECTO: SUBESTACIÓN Y DISTRIBUCIÓN ELÉCTRICA - EDIFICIO CORPORATIVO

PLANO 1: DIAGRAMA UNIFILAR - TABLERO GENERAL DE DISTRIBUCIÓN (480V / 277V, 3F, 4H)

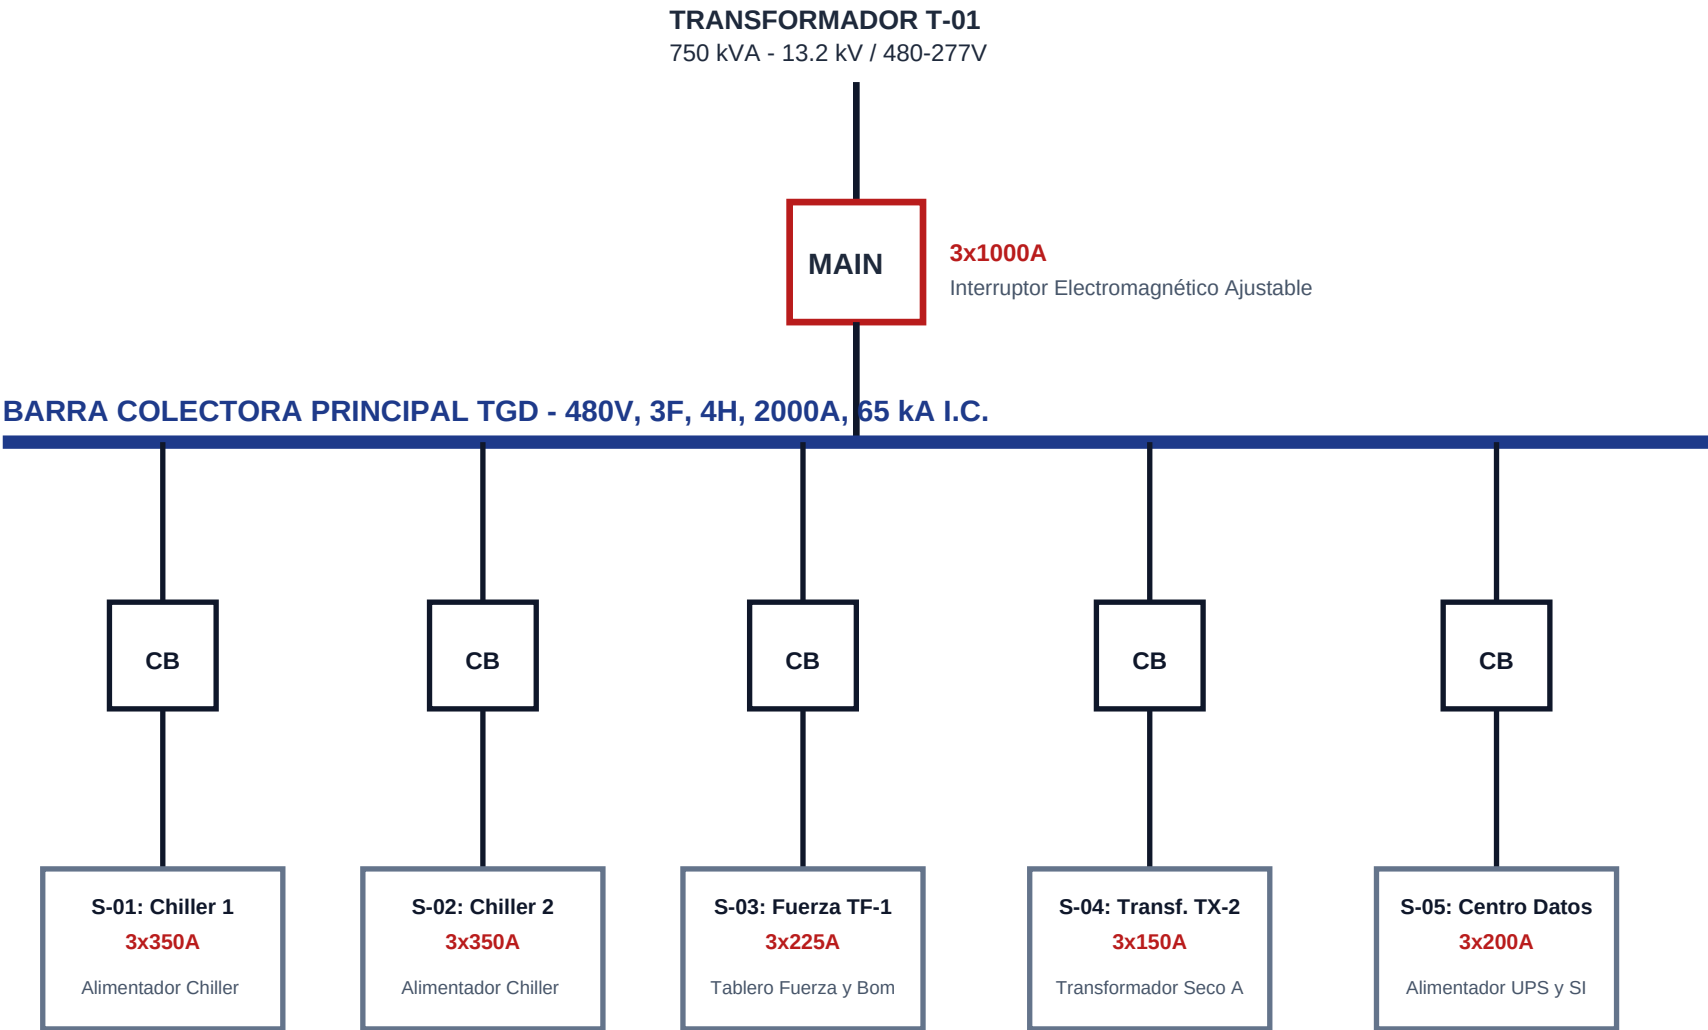

NOTAS DE SUBMEDICIÓN Y AUDITORÍA ENERGÉTICA:

- Medir acometida principal en bornes de carga del interruptor MAIN.
- Medir cada alimentador de primer nivel derivado de la barra colectora.
- Emplear TCs de núcleo partido con salida 0-333mV o donas Rogowski.

PROYECTO: SUBESTACIÓN Y DISTRIBUCIÓN ELÉCTRICA - EDIFICIO CORPORATIVO

PLANO 2: DIAGRAMA UNIFILAR - SISTEMA DE EMERGENCIA Y PLANTA ELÉCTRICA

